


SCHEDULE OF FOOTINGS

FOOTING MARK	SIZE			BOTTOM REINFORCEMENT	
	LENGTH (L)	WIDTH (W)	DEPTH (D)	A	B
F1	2800	2600	600	Y12@100	Y12@100
F2	3000	2800	600	Y12@100	Y12@100
F2A	2500	2800	750	Y16@150	Y16@150
F3	3200	3000	750	Y12@125	Y12@125
F4	3600	3400	750	Y16@150	Y16@150
CF1	REFER PLAN 600 THK.	BOTTOM	TOP	Y12@150	Y12@150
			BOTTOM	Y16@150	Y16@150
CF2	REFER PLAN 750 THK.	BOTTOM	TOP	Y16@175	Y16@175
			BOTTOM	Y16@150	Y16@150
CF3	REFER PLAN 750 THK.	BOTTOM	TOP	Y16@175	Y16@125
			BOTTOM	Y16@100	Y16@100


NOTES:

- GRADE OF CONCRETE SHALL BE M25 FOR ALL R.C.C WORKS.
- T/Y DENOTES HYSD TMT BARS OF GRADE Fe 500 CONFORMING TO IS 1786-1985.
- LAP LENGTH SHALL BE 50 TIMES DIA OF THE BAR AND TO BE STAGGERED SUCH THAT NOT MORE THAN 50% OF THE BARS ARE LAPPED AT A SECTION.
- CLEAR COVER TO THE REINFORCEMENT :
FOOTING/WALL : 50 mm
COLUMNS : 40 mm
SLAB : 20 mm
BEAM : 25 mm
- DEVELOPMENT LENGTH SHALL BE 50 TIMES THE DIA. OF THE BAR.
- S.B.C OF SOIL CONSIDERED IS 23.0 T/m²
- STRUCTURE IS DESIGNED FOR GROUND+8 STORES ONLY

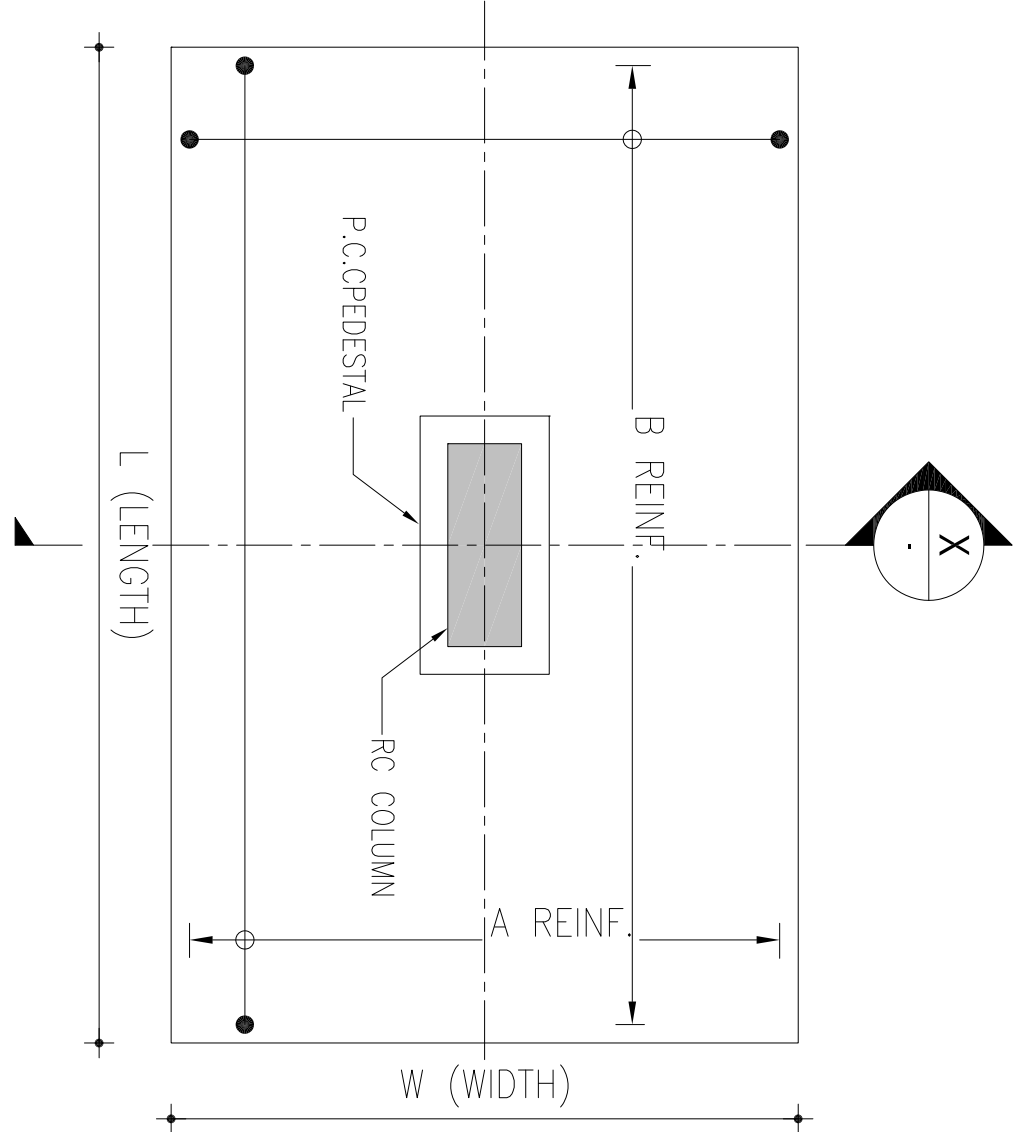

2 TYPICAL PLAN OF FOOTING

SCALE 1:20

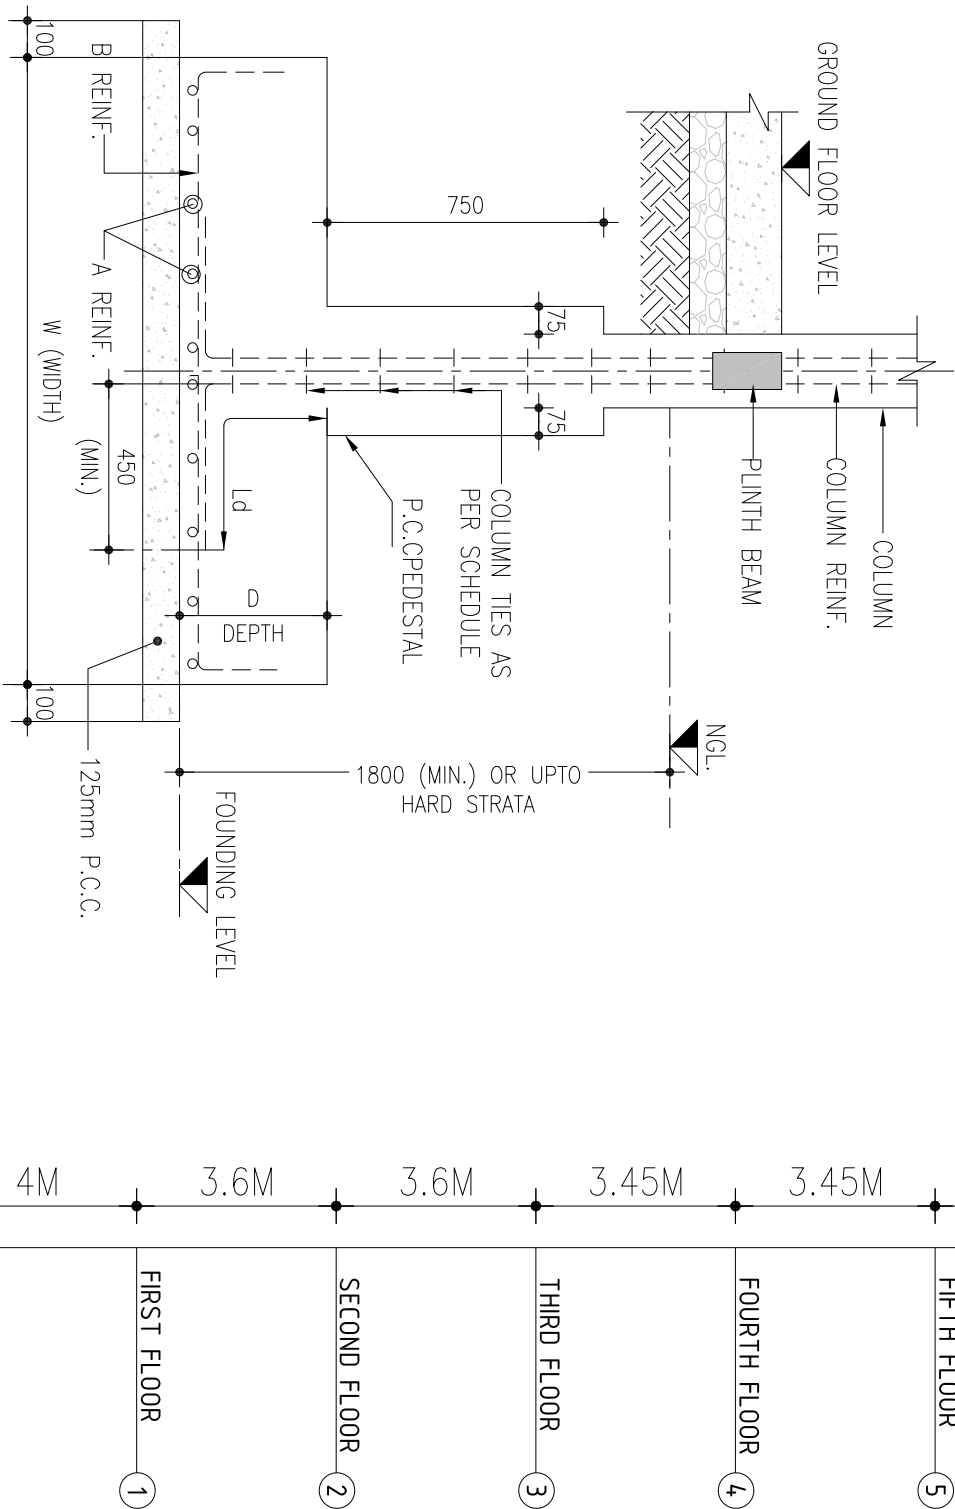


3 SECTION X

SCALE 1:20

(FOR DIMENSIONS REFER TO FOOTING SCHEDULE)

DESIGNED FOR G+8 FLOORS+ TERRACE (9 SLABS)

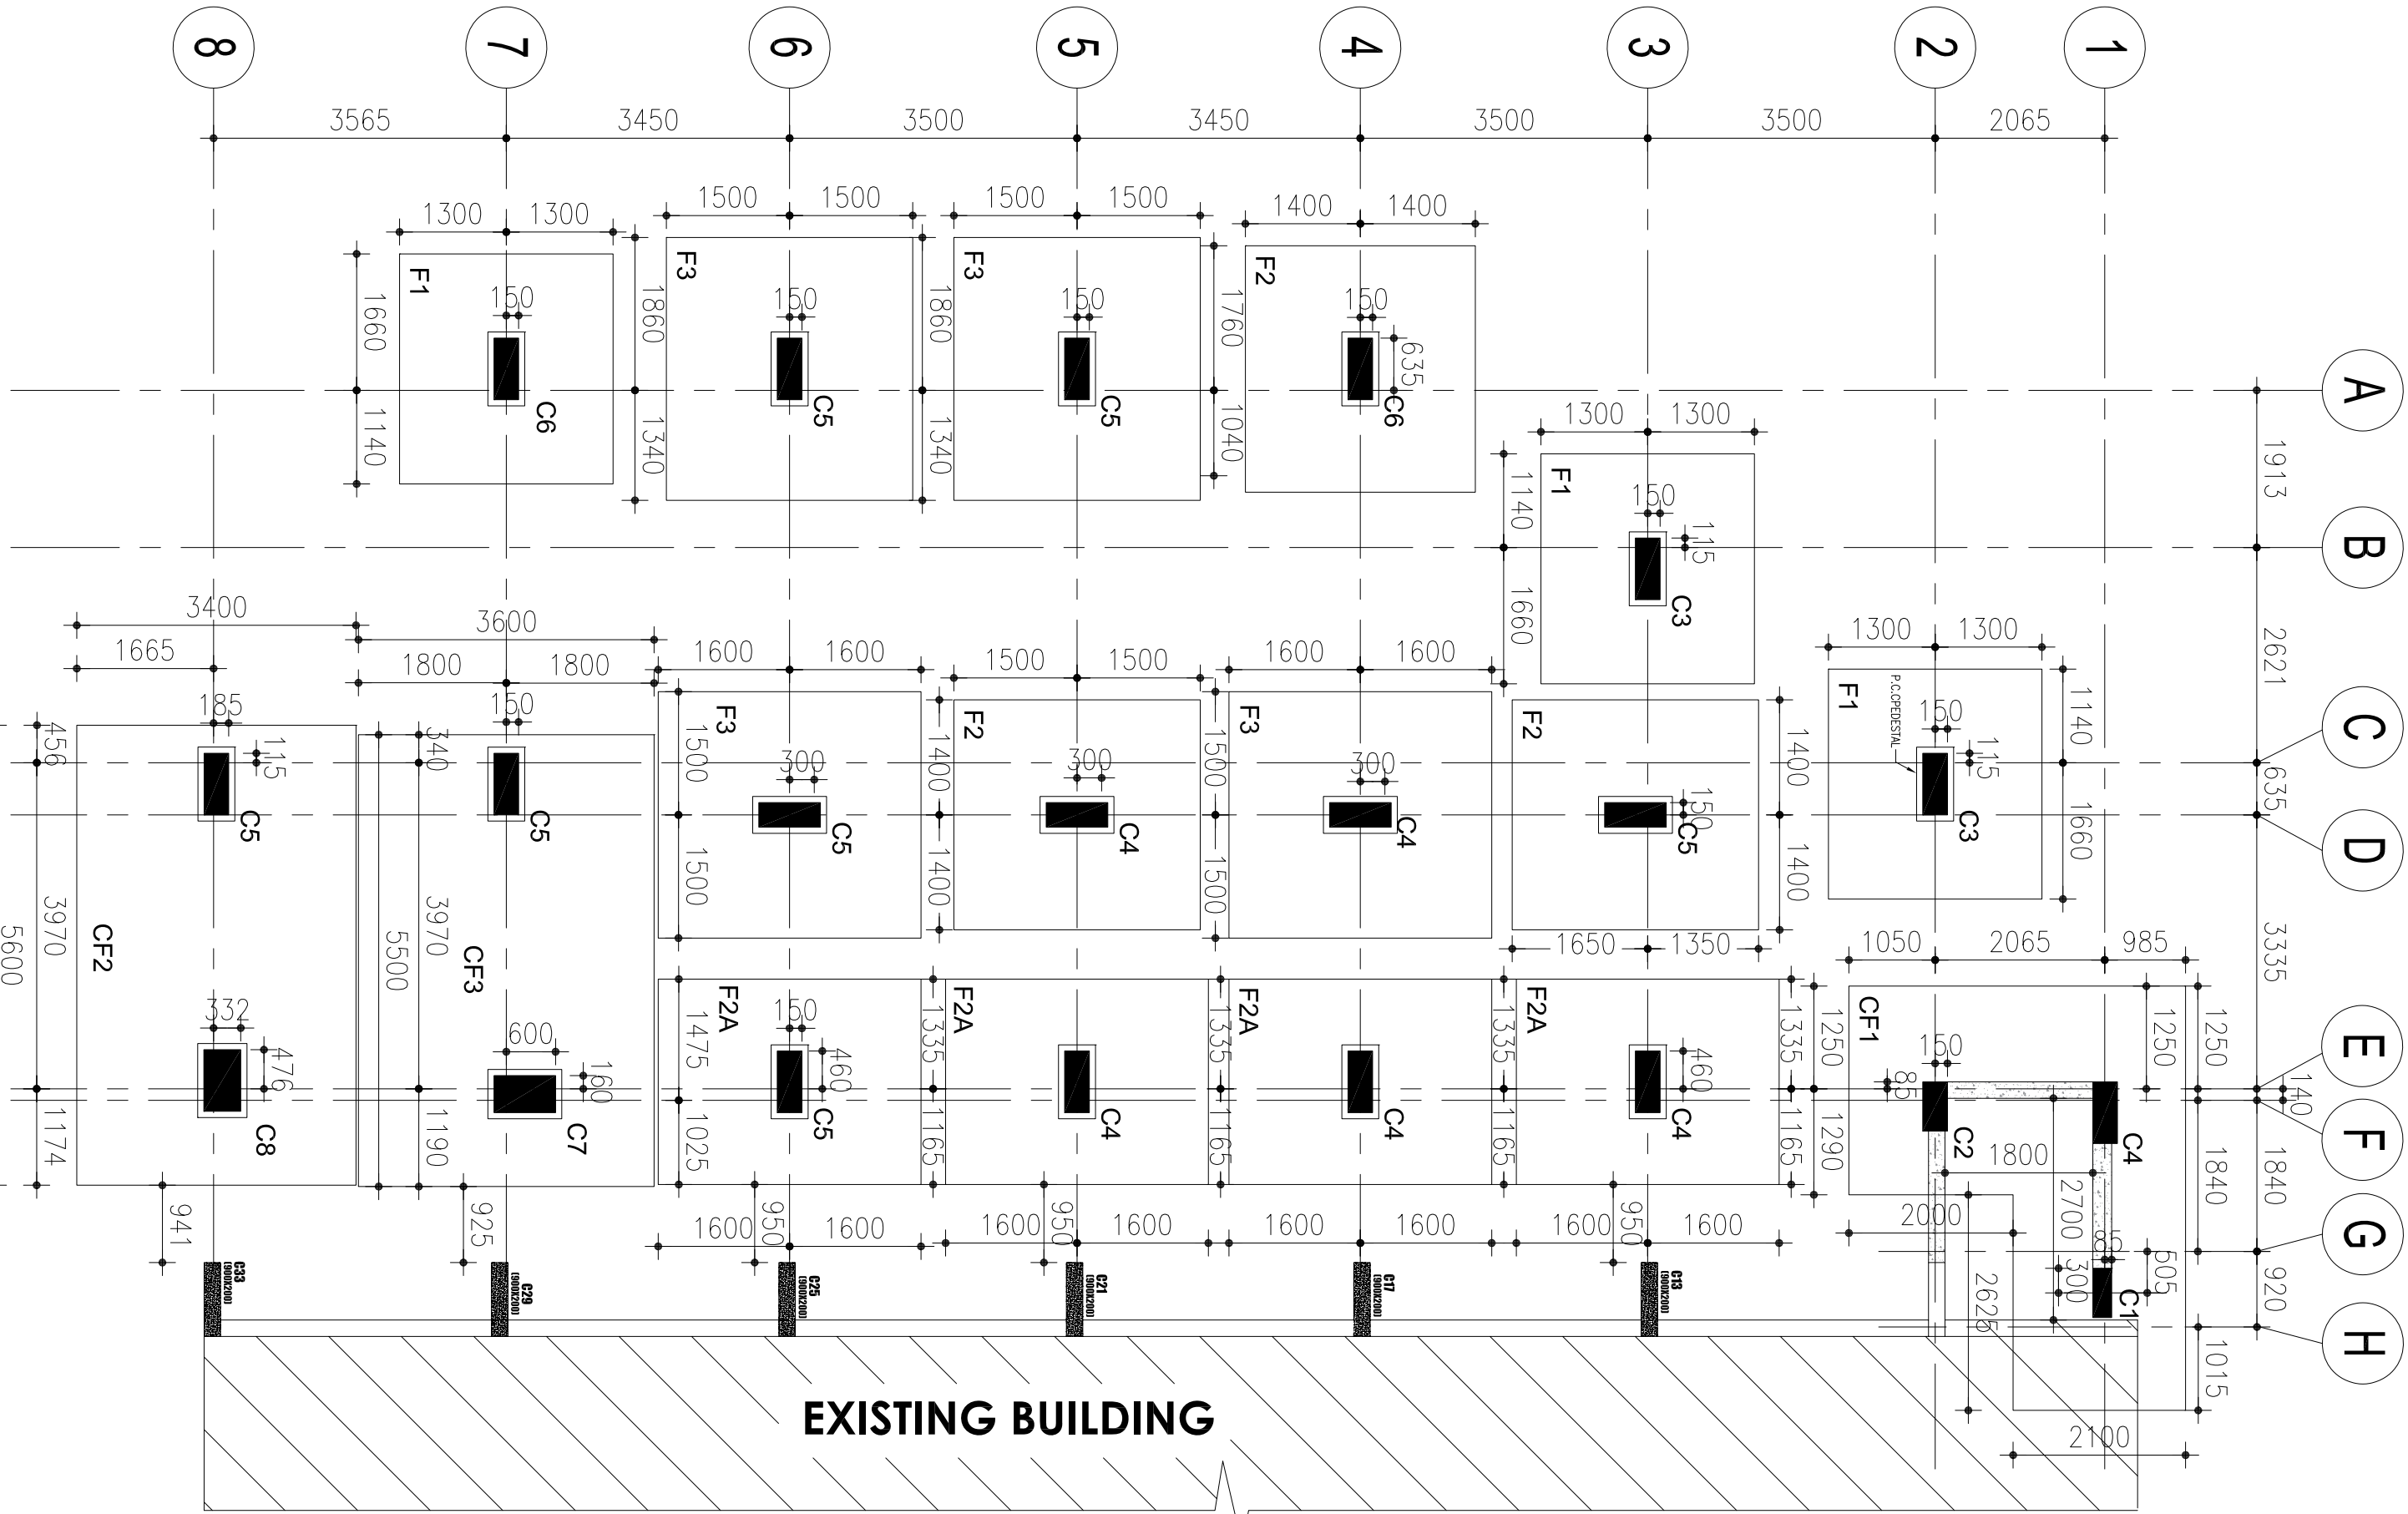

1 FOUNDATION LAYOUT

SCALE 1:75

- NOTES:
- ALL FOOTINGS ARE SYMMETRICAL ABOUT COLUMN (U.N.O.).
 - FOR SETTING-OUT OF GRIDS REFER RELEVANT ARCH. SETTING-OUT DRAWING.
 - IF LOOSE PATCHES FOUND SUITABLE THICKNESS OF BOULDER FILLING SHALL BE PROVIDED.

	SIXTH FLOOR TO TERRACE LVL.	FOURTH FLOOR TO SIXTH FLOOR LVL.	SECOND FLOOR TO FOURTH FLOOR LVL.	FOUNDATION TO SECOND FLOOR LVL.	COLUMN MARK
SECTION X					C1
					C2
					C3
					C4
					C5
SECTION Y					C6
					C7
					C8
					C9
					C10

GENERAL NOTES:

- DO NOT SCALE FROM THE DRAWINGS. FOLLOW WRITTEN DIMENSIONS ONLY.
- ALL DIMENSIONS ARE IN MILLIMETERS AND LEGS IN METERS (UNLESS NOTED OTHERWISE, ALL DIMENSIONS TO BE VERIFIED ON SITE BEFORE EXECUTION & APPROVED BY THE ENGINEER.
- THIS DRAWING SHOULD BE READ IN CONJUNCTION WITH OTHER RELEVANT ARCHITECTURAL, STRUCTURAL, MECHANICAL, ELECTRICAL AND CIVIL DRAWINGS AND ALL RELEVANT SECTIONS OF THE SPECIFICATIONS.
- EXECUTION OF THE WORKS SHALL BE CARRIED BY QUALIFIED PERSONNEL ONLY. ANY DISCREPANCY IN SITE SHALL BE BROUGHT TO THE NOTICE OF THE CONSULTANTS PRIOR TO THE EXECUTION.

Drawn by :-	AIJ	Scale :-	AM
Check by :-	PVS		
Issued for :-			
Project :-	GOOD FOR CONSTRUCTION		
Sheet Description :-	CANTEEN EXTENSION BUILDING		
Comments :-			
FOUNDATION DETAILS			
Project Name :-	Drawing No :- CC020202SSD-001		